FINAL PLAT

GIBBONS PARK ESTATES SUBDIVISION

LOCATED IN THE NE 1/4 OF SECTION 2, TOWNSHIP 12 NORTH, RANGE 1 EAST, SALT LAKE BASE AND MERIDIAN. LOGAN CITY, CACHE COUNTY, UTAH.

SCALE 1" = 40'


OWNER/SUBDIVIDER
GIBBONS PARK ESTATES, LLC
55 South 900 West STE 1A
Hyde Park, Utah 84318

PLAT NOTES:


1. #5 REBAR & CAP TO BE SET AT ALL BOUNDARY CORNERS. CURB PINS TO BE SET IN THE TOP OF THE CURB AT THE EXTENSION OF THE SIDE LOT LINES.

UTILITY NOTES:

1. ENBRIDGE GAS INC. APPROVES THIS PLAT SOLELY FOR THE PURPOSE OF CONFORMING THAT THE PLAT CONTAINS PUBLIC UTILITY EASEMENTS. ENBRIDGE MAY REQUIRE ADDITIONAL EASEMENTS IN ORDER TO SERVE THIS DEVELOPMENT. THIS APPROVAL DOES NOT CONSTITUTE ABROGATION OR WAIVER OF ANY EXISTING RIGHTS, OBLIGATIONS OR LIABILITIES PROVIDED BY LAW OR EQUITY. THIS APPROVAL DOES NOT CONSTITUTE ACCEPTANCE, APPROVAL OR ACKNOWLEDGMENT OF ANY TERMS CONTAINED IN THIS PLAT, INCLUDING THOSE SET IN THE OWNER'S DEDICATION AND THE NOTES AND DOES NOT CONSTITUTE A GUARANTEE OF PARTICULAR TERMS OF NATURAL GAS SERVICE.
2. PURSUANT TO UTAH CODE ANN. §54-3-27 THIS PLAT CONVEYS TO THE OWNER(S) OR OPERATORS OF UTILITY FACILITIES A PUBLIC UTILITY EASEMENT ALONG WITH ALL THE RIGHTS AND DUTIES DESCRIBED THEREIN.
3. ALL STORM WATER STRUCTURES OUTSIDE OF LOGAN CITY RIGHT-OF-WAY AND OUTSIDE OF LOGAN CITY PROPERTY IS TO BE OWNED AND MAINTAINED BY THE PROJECT HOA.
4. THE STORM WATER DETENTION EASEMENT AS SHOWN ON LOT 1 AND LOT 10 ARE DEDICATED TO THE PROJECT HOA TO GIVE ACCESS FOR LONG-TERM OPERATION INCLUDING INSPECTION, MAINTENANCE AND REPAIR OF THE STORM WATER INFRASTRUCTURE.

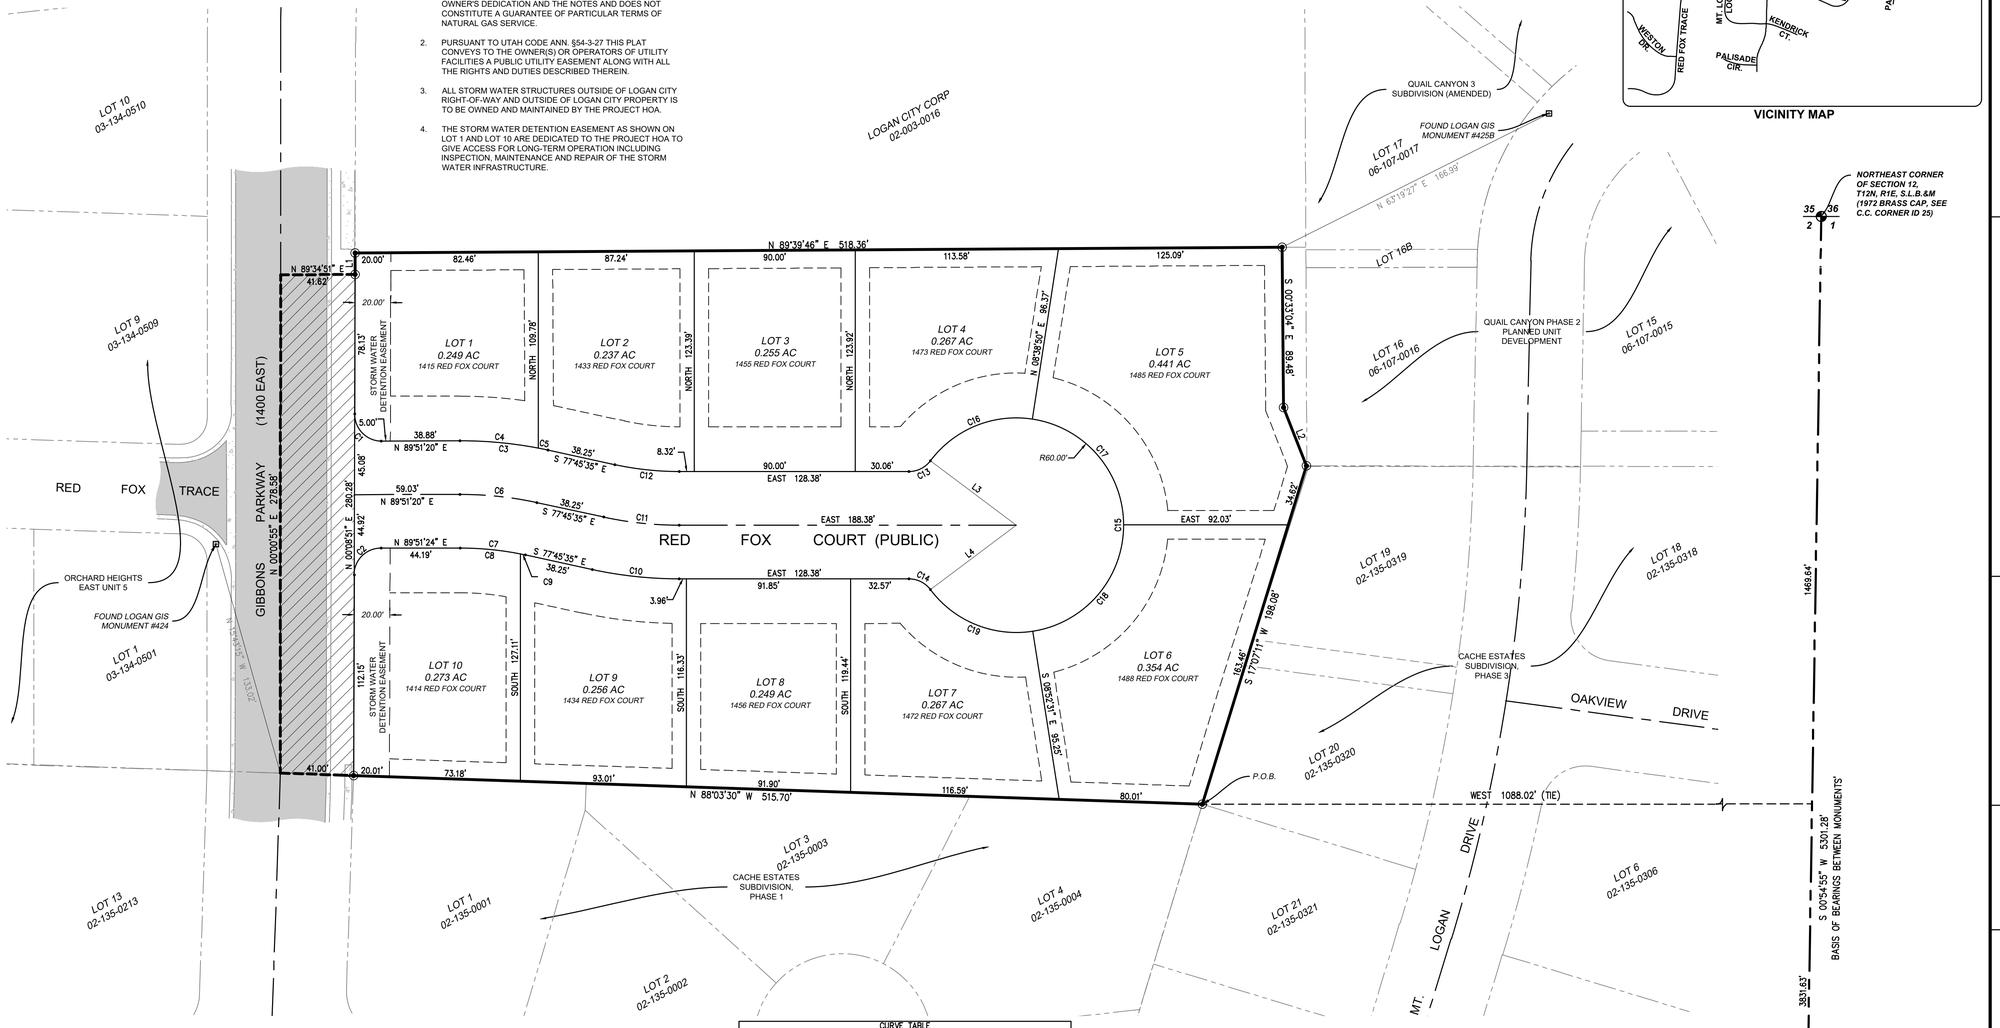

VICINITY MAP

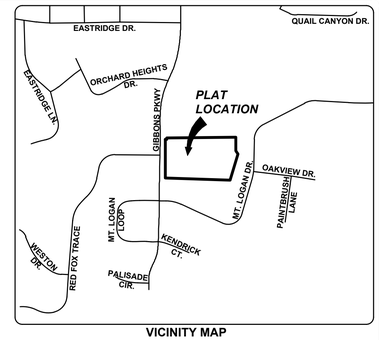

LEGEND

- EXTERIOR PROPERTY CORNER
- FOUND SECTION CORNER (SEE MAP FOR DETAILS)
- PROPERTY BOUNDARY
- ADJOINING PROPERTY LINES
- SECTION LINES
- PLATTED ROAD CENTERLINES
- BUILDING SETBACK
- CONCRETE SIDEWALK / CURB & GUTTER
- ASPHALT ROADWAY
- AREA DEDICATED TO LOGAN CITY FOR GIBBONS PARKWAY. 0.265 AC


CURVE TABLE

CURVE	RADIUS	ARC LENGTH	DELTA ANGLE	CHORD LENGTH	CHORD BEARING
C1	15.00'	23.56'	90°00'30.57"	21.21'	S 44°51'24" E
C2	15.00'	23.56'	89°59'29.43"	21.21'	N 45°08'36" E
C3	230.00'	49.72'	12°23'04.76"	49.62'	S 83°57'07" E
C4	230.00'	44.11'	10°59'15.21"	44.04'	S 84°39'02" E
C5	230.00'	5.61'	1°23'49.55"	5.61'	S 78°27'30" E
C6	200.00'	43.23'	12°23'04.76"	43.15'	S 83°57'07" E
C7	170.00'	36.75'	12°23'04.76"	36.67'	S 83°57'07" E
C8	170.00'	33.84'	11°24'15.58"	33.78'	S 84°26'32" E
C9	170.00'	2.91'	0°58'49.18"	2.91'	S 78°15'00" E
C10	230.00'	49.14'	12°14'24.89"	49.04'	S 83°52'48" E
C11	200.00'	42.73'	12°14'24.89"	42.65'	S 83°52'48" E
C12	170.00'	36.32'	12°14'24.89"	36.25'	S 83°52'48" E
C13	15.00'	13.91'	53°07'48.33"	13.42'	N 63°26'06" E
C14	15.00'	13.91'	53°07'48.40"	13.42'	S 63°26'06" E
C15	60.00'	299.77'	286°15'36.72"	72.00'	SOUTH
C16	60.00'	64.69'	61°46'38.76"	61.60'	N 67°45'31" E
C17	60.00'	85.08'	81°14'46.26"	78.13'	S 40°43'46" E
C18	60.00'	83.06'	81°31'51.94"	76.12'	S 40°30'13" W
C19	60.00'	64.93'	62°00'19.77"	61.81'	N 67°52'21" W

LINE TABLE

LINE	BEARING	DISTANCE
L1	N 00°09'11" E	12.02'
L2	S 21°21'36" E	35.06'
L3	N 53°07'48" W	60.00'
L4	S 53°07'48" W	60.00'

PUE & SETBACK DETAIL

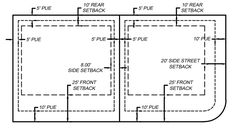

SURVEYOR'S CERTIFICATE

I, KEVIN M. BALLS, DO HEREBY CERTIFY THAT I AM A PROFESSIONAL LAND SURVEYOR, AND THAT I HOLD LICENSE NO. 11207308-2201 IN ACCORDANCE WITH TITLE 58, CHAPTER 22 OF UTAH STATE CODE. I FURTHER CERTIFY BY AUTHORITY OF THE OWNER(S) THAT I HAVE COMPLETED A SURVEY OF THE PROPERTY DESCRIBED ON THIS PLAT IN ACCORDANCE WITH SECTION 17-23-17 OF SAID CODE, AND HAVE ALSO SUBDIVIDED SAID TRACT OF LAND INTO LOTS, STREETS, AND EASEMENTS, AND THE SAME HAS, OR WILL BE CORRECTLY SURVEYED, STAKED AND MONUMENTED ON THE GROUND AS SHOWN ON THIS PLAT.

KEVIN M. BALLS
PROFESSIONAL LAND SURVEYOR
LICENSE NO. 11207308-2201

BOUNDARY DESCRIPTION

BEGINNING AT THE NORTHEAST CORNER OF LOT 4, CACHE ESTATES SUBDIVISION PHASE 1, FILED IN THE CACHE COUNTY RECORDER'S OFFICE AS ENTRY NO. 584356, SAID CORNER BEING S00°54'55"W 1469.94 FEET MEASURED ON A LINE BETWEEN THE NORTHEAST AND SOUTHEAST CORNERS OF SECTION 12, AND WEST 1088.22 FEET FROM THE 1972 BRASS CAP MONUMENT MARKING THE NORTHEAST CORNER OF SECTION 12, TOWNSHIP 12 NORTH, RANGE 1 EAST, SALT LAKE BASE AND MERIDIAN;
AND RUNNING THENCE N88°03'30"W 515.70 FEET ALONG THE NORTH BOUNDARY OF SAID CACHE ESTATES SUBDIVISION PHASE 1; THENCE N00°00'55"E 278.58 FEET ALONG THE CENTERLINE OF GIBBONS PARKWAY; THENCE N89°34'51"E 41.63 FEET; THENCE N00°09'11"E 12.02 FEET ALONG THE SURVEYED BOUNDARY PER THAT CERTAIN RECORD OF SURVEY PERFORMED BY RANDALL J. WILLIFORD (REEVE & ASSOCIATES, INC.) FILE NO. 2001-0054; THENCE N89°39'46"E 516.36 FEET; THENCE S00°33'04"E 89.48 FEET; THENCE S21°21'36"E 35.06 FEET TO THE NORTHWEST SUBDIVISION CORNER OF CACHE ESTATES SUBDIVISION PHASE 3, FILED IN THE CACHE COUNTY RECORDER'S OFFICE AS ENTRY NO. 620928; THENCE S17°07'11"W 198.08 FEET ALONG SAID SUBDIVISION TO THE POINT OF BEGINNING.

CONTAINS 3.807 ACRES.

THE BASIS OF BEARINGS FOR THIS PLAT WAS ESTABLISH AS S 00°54'55"W 5301.28' FEET MEASURED BETWEEN THE NORTHEAST AND SOUTHEAST CORNERS OF SECTION 2, TOWNSHIP 12 NORTH, RANGE 1 EAST, SALT LAKE BASE AND MERIDIAN.

OWNER'S DEDICATION

KNOW ALL MEN BY THESE PRESENTS THAT WE, THE UNDERSIGNED OWNERS OF THE TRACT OF LAND DEPICTED AND DESCRIBED HERON, HAVE CAUSED THE SAME TO BE SUBDIVIDED INTO LOTS AND STREETS, TOGETHER WITH EASEMENTS AS SETFORTH TO BE HEREAFTER KNOWN AS:

GIBBONS PARK ESTATES SUBDIVISION

AND DO HEREBY DEDICATE GRANT AND CONVEY TO LOGAN CITY, UTAH ALL THOSE PARTS OR PORTIONS OF SAID TRACT OF LAND DESIGNATED AS STREETS. THE SAME TO BE USED AS PUBLIC THOROUGHFARES FOREVER, AND DO ALSO DEDICATE TO LOGAN CITY THOSE CERTAIN STRIPS AS EASEMENTS FOR PUBLIC UTILITY PURPOSES AS SHOWN HEREON. THE SAME TO BE USED FOR THE INSTALLATION, MAINTENANCE AND OPERATION OF PUBLIC UTILITY SERVICE LINES AS INTENDED FOR PUBLIC USE.

IN WITNESS WHEREOF WE HAVE HEREUNTO SET OUR HANDS THIS ____ DAY OF _____, 20____.

MAMMOTH GROUP, LLC

BY:_____(SIGNATURE)

ITS: _____

ACKNOWLEDGEMENT

STATE OF UTAH
COUNTY OF CACHE

ON THIS _____DAY OF _____, 20____, PERSONALLY APPEARED BEFORE ME, _____ WHOSE IDENTITIES ARE PERSONALLY KNOWN TO ME (OR PROVEN ON THE BASIS OF SATISFACTORY EVIDENCE) AND WHO BY ME DULY SWORE/AFFIRMED, DID SAY THAT THEY ARE THE PERSONS WHOSE NAMES ARE SUBSCRIBED TO THIS INSTRUMENT, AND ACKNOWLEDGE THAT THEY EXECUTED THE SAME.

_____
NOTARY PUBLIC (SIGNATURE)

MAYOR APPROVAL & ACCEPTANCE

PRESENTED TO THE LOGAN CITY MAYOR THIS _____ DAY OF _____, 20____, AT WHICH TIME THE SUBDIVISION WAS APPROVED AND ACCEPTED.

_____ LOGAN CITY MAYOR
_____ ATTEST

PLANNING COMMISSION APPROVAL

THIS SUBDIVISION ENTERED INTO CITY RECORDS AS PLANNING COMMISSION DOCKET # PC 25-028 WAS HEARD BEFORE THE COMMISSION IN A PUBLIC HEARING ON THE 24TH DAY OF APRIL, 2025 , AND WAS APPROVED IN SUBSTANTIAL CONFORMANCE WITH THE REQUIREMENTS AND DESIGN SHOWN UPON THIS PLAT MAP.

_____ DIRECTOR OF COMMUNITY DEVELOPMENT
_____ DATE

GIBBONS PARK ESTATES SUBDIVISION

LOCATED IN THE NE 1/4 OF SECTION 2, TOWNSHIP 12 NORTH, RANGE 1 EAST, SALT LAKE BASE AND MERIDIAN. LOGAN CITY, CACHE COUNTY, UTAH.

COUNTY RECORDER

STATE OF UTAH
COUNTY OF CACHE

THIS PLAT HAS BEEN DULY ACKNOWLEDGED, CERTIFIED, AND APPROVED AND MAY LAWFULLY BE RECORDED IN CACHE COUNTY, UTAH.

FILED AND RECORDED:_____

FILING NO.:_____

DATE: _____ TIME: _____ BOOK: _____ PAGE: _____

REQUEST OF:_____

_____
COUNTY RECORDER

ALPENGLOW ENGINEERS & SURVEYORS, LLC
Serving Northern Utah and Surrounding areas.
Phone: 435.512.4559
office@alpenglow-es.com

PROJECT #:	25-013
DRAWN BY:	KMB
SCALE:	1" = 40'
DATE:	02-09-2026

SHEET 1 OF 1

LOGAN CITY ENGINEER'S APPROVAL

I CERTIFY THAT I HAVE EXAMINED THIS PLAT AND FIND IT TO BE CORRECT AND IN ACCORDANCE WITH THE INFORMATION ON FILE IN THIS OFFICE AND THE CITY ORDINANCE.

_____ CITY ENGINEER
_____ DATE

LOGAN CITY ATTORNEY APPROVAL

APPROVED AS TO FORM THIS _____ DAY OF _____, 20____.

_____ CITY ATTORNEY

LOGAN CITY UTILITIES

_____ WATER _____ DATE
_____ SOLID WASTE _____ DATE
_____ WASTE WATER COLLECTION _____ DATE
_____ LIGHT & POWER _____ DATE
_____ WASTE WATER TREATMENT _____ DATE